Seiler Residence
1st Floor Construction Plan

13 May 2025 : Seiler Residence_1st Floor Construction Plan

Summary Report

CUSTOM FLOORING & INTERIORS, INC
COMMERCIAL & RETAIL SPECIALIST

area	net	gross	waste	perimeter	base
WD1 - 5" Wood Flooring : 6'x5.00" [split 202:full 232] [tileEdge= 1902'1.0"]					342 5.00"x6' [855.00sf]
area count=1	**755.98sf**	**855.00sf**	**13.10%**	**312'3.2"**	
CPT1 - Carpet Flooring : width 12': cutTol3.00": seam 10'0.6"					[12'] x [53'1.1"] gross
area count=3	**53.13sy**	**70.79sy**	**33.23%**	**199'5.3"**	
Wood to Carpet Transition					
area count=1	**0.00sy**	**0.00sy**			**7'11.5"**
Plan Total	**137.13sy**			**511'8.5"**	
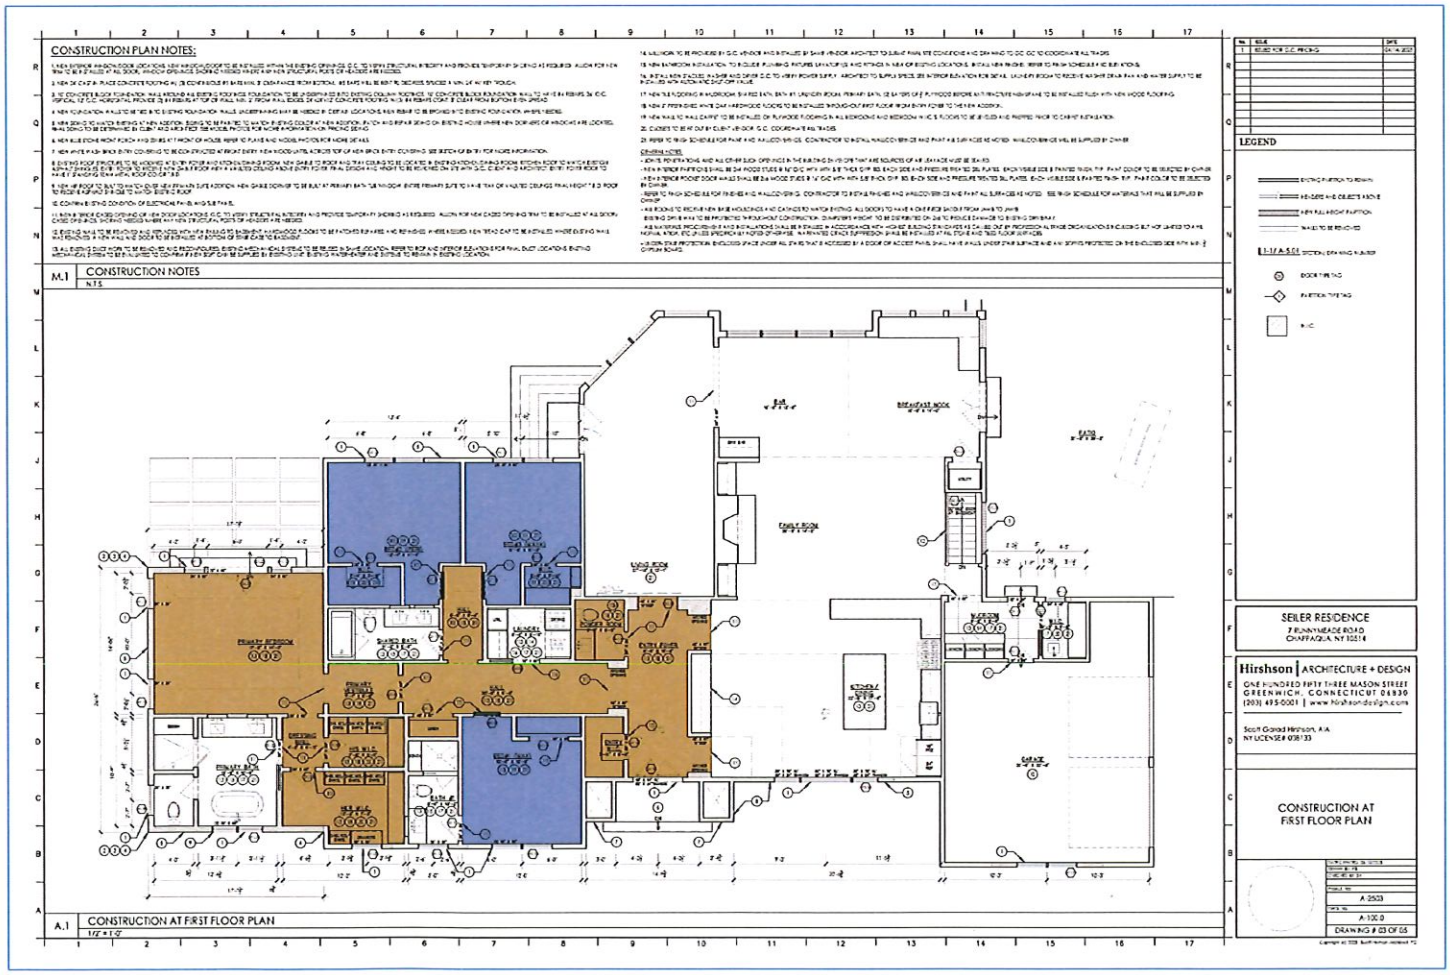
Scale 1:230 (original drawing scale 1:48)