Soloman Residence
1st Floor Construction Plan

13 May 2025 : Soloman Residence_1st Floor Construction Plan

Summary Report

CUSTOM FLOORING & INTERIORS, INC
COMMERCIAL & RETAIL SPECIALIST

area	net	gross	waste	perimeter	base
WD1 - 5" Wood Flooring : 6'x5.00" [split 148:full 372] [tileEdge= 2707'5.2"]					468 5.00"x6' [1170.01sf]
area count=1	1063.94sf	1170.01sf	9.97%	195'10.3"	
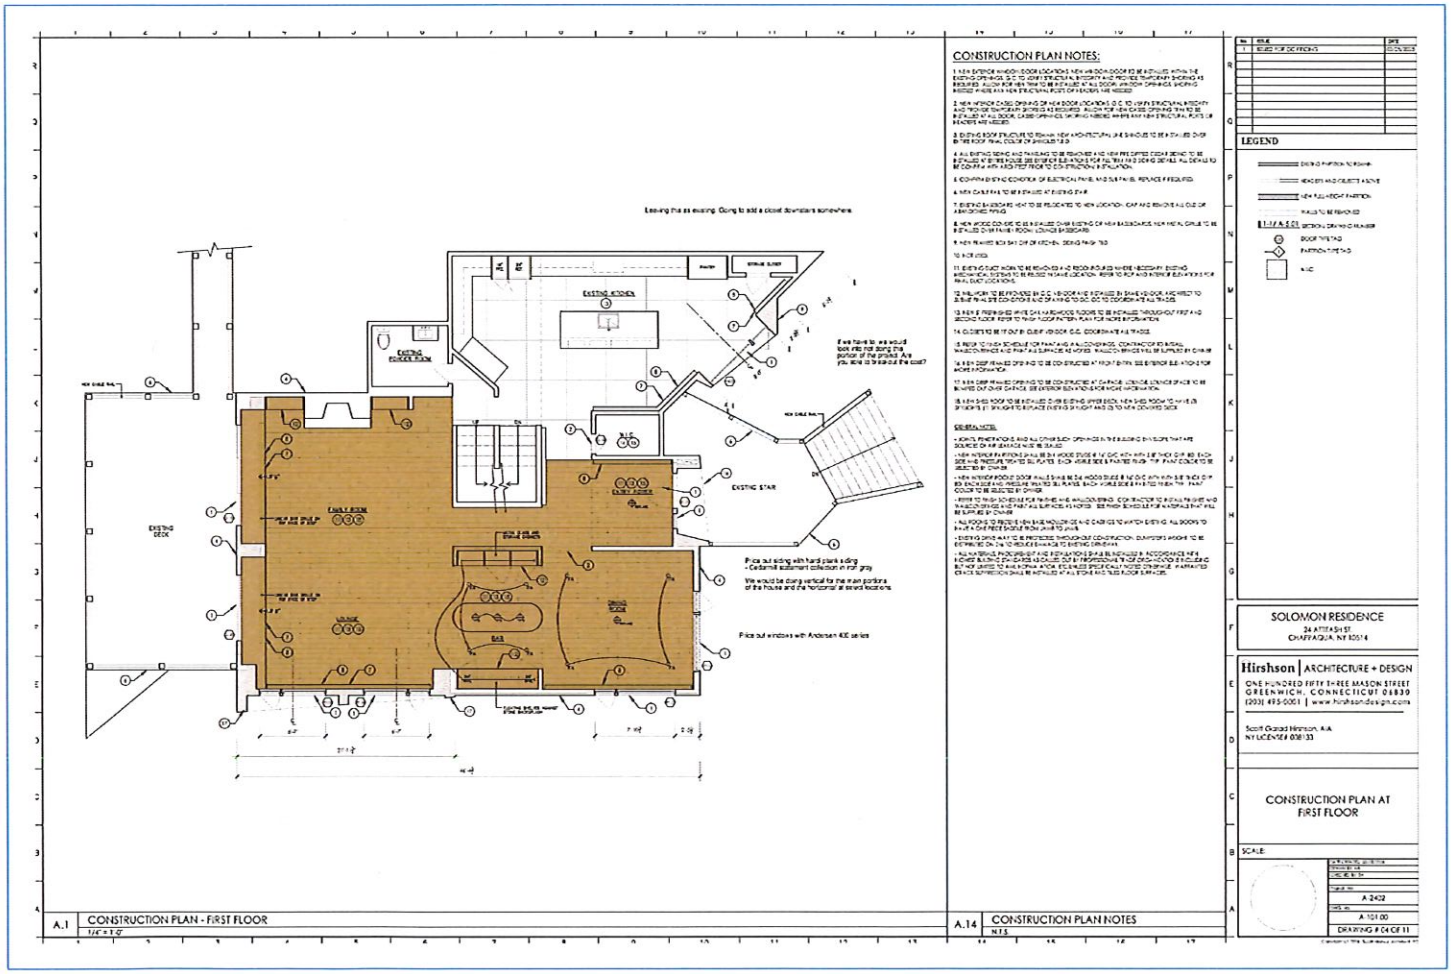
Scale 1:230 (original drawing scale 1:48)