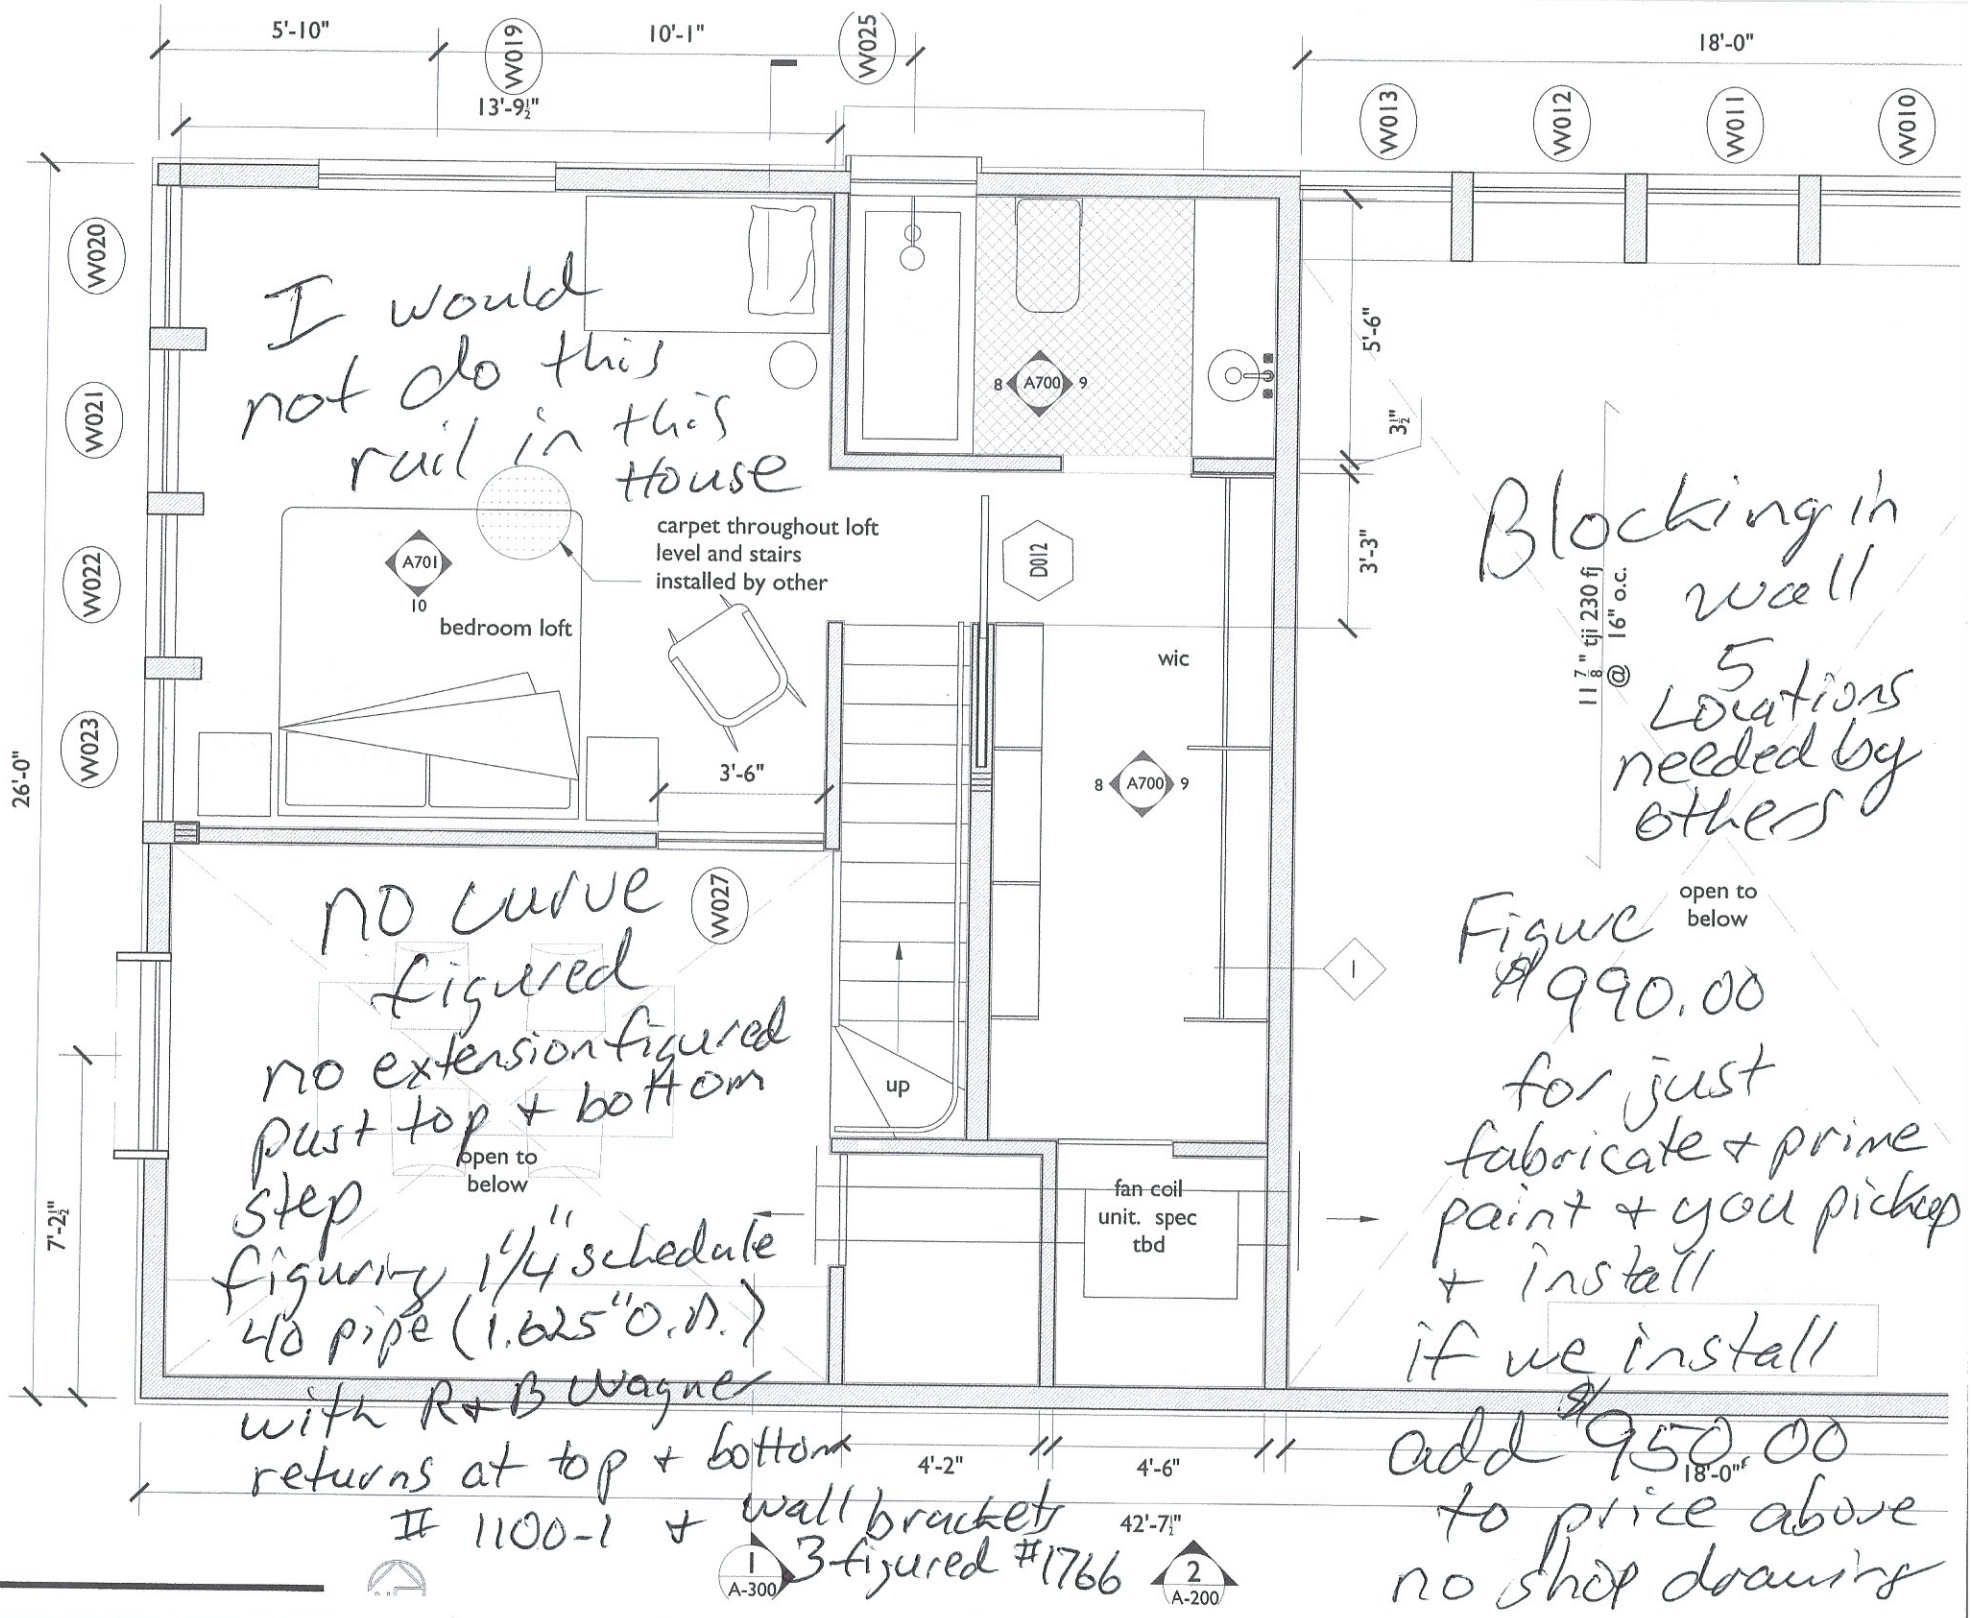
5'-10"
W019
10'-1"
W025
13'-9½"
18'-0"
W013
W012
W011
W010
W020
W021
W022
W023
26'-0"
I would not do this rail in this house
A700
8
9
5'-6"
3½"
3'-3"
carpet throughout loft level and stairs installed by other
A701
10
bedroom loft
D012
wic
11 7/8" tji 230 fj @ 16" o.c.
Blocking in wall 5 Locations needed by others
3'-6"
A700
8
9
open to below
Figure $990.00 for just fabricate + prime paint + you pickup + install
W027
no curve figured
no extension figured
must top + bottom step
figuring 1¼" schedule 40 pipe (1.625" O.D.)
open to below
1
up
fan coil unit. spec tbd
7'-2½"
with R+B Wagner returns at top + bottom
1100-1 + wall brackets 3-figured #1766
add $950.00 to price above no shop drawing
4'-2"
4'-6"
18'-0"
42'-7½"
1
A-300
2
A-200
I plan