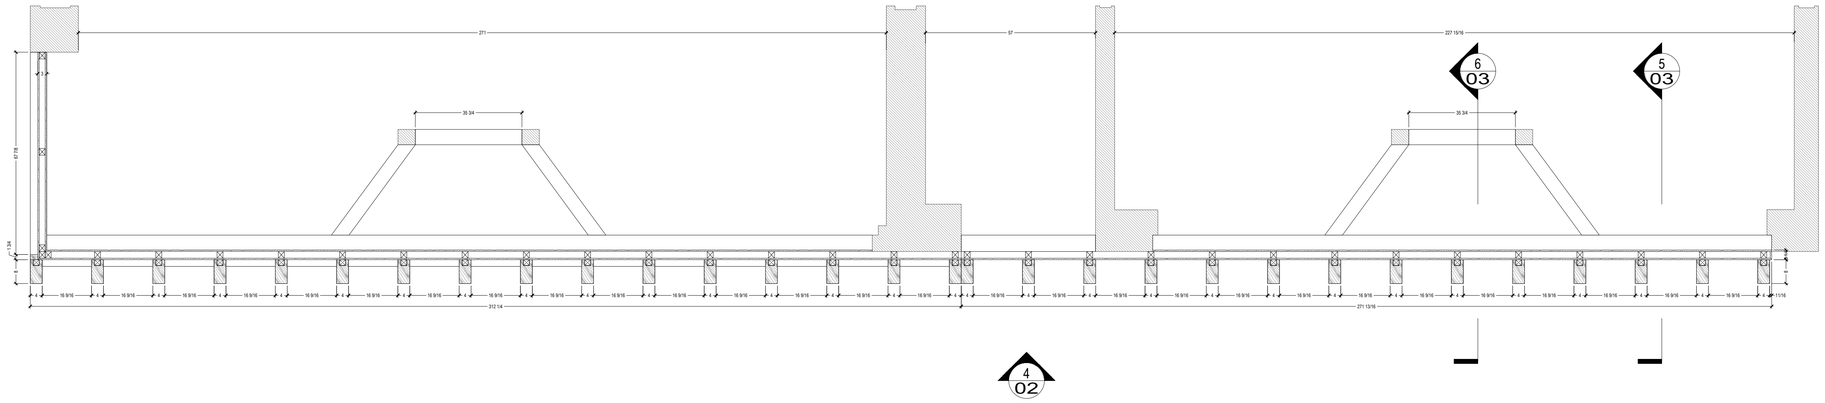


3 STOREFRONT PLAN @ C
SCALE: 1/2"=1'-0"

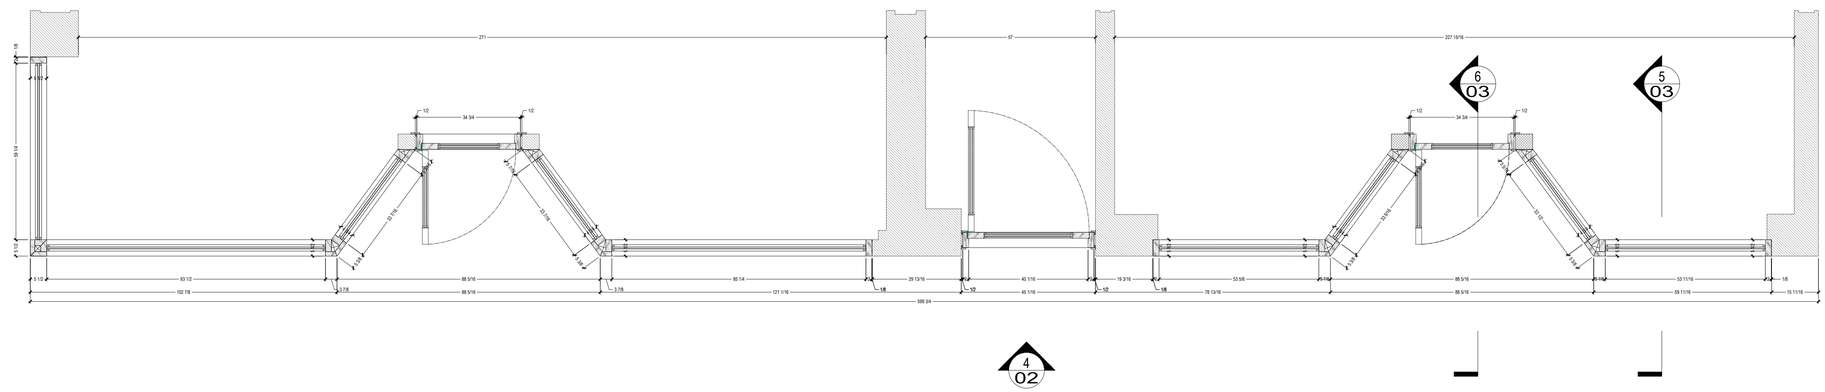


2 STOREFRONT PLAN @ B
SCALE: 1/2"=1'-0"

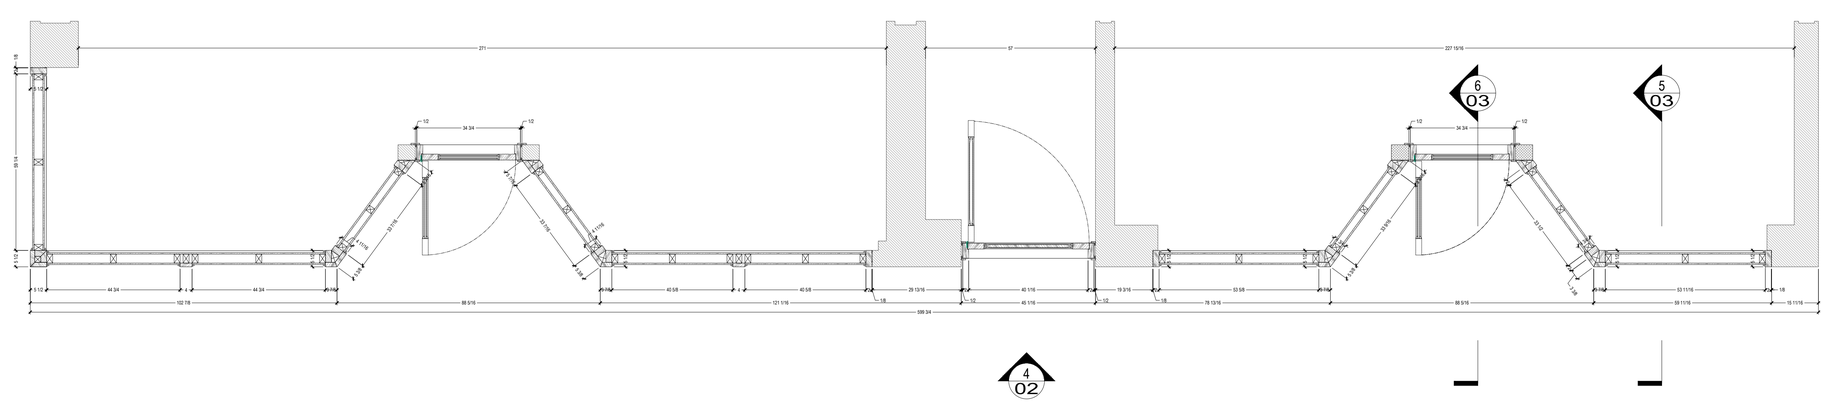


1 STOREFRONT PLAN @ A
SCALE: 1/2"=1'-0"

WD 01
WOOD FRAME
STOREFRONT (AS PER
APPROVED SAMPLE)

PROJECT:

SHOPFRONT
ADDRESS
ADDRESS
ADDRESS

FX-X_TITLE
RM#_Title

| REVISIONS | BY |
|---|---|
| | |
| | |

ENG: ----
FIN: ----
PM: ----
DATE: NOV. 06, 2025
JOB # 00-00-00000
ARCH REF. T-REF
B-REF

SHEET
01

4 ELEVATION
SCALE: 1/2"=1'-0"

WD 01
WOOD FRAME
STOREFRONT (AS PER
APPROVED SAMPLE)

PROJECT:
SHOPFRONT
ADDRESS
ADDRESS
ADDRESS

FX-X_TITLE

| REVISIONS | BY |
|---|---|
| | |
| | |

ENG: ----
FIN: ----
PM: ----
DATE: NOV. 06, 2025
JOB # 00-00-00000
ARCH REF. T-REF
B-REF

SHEET
02

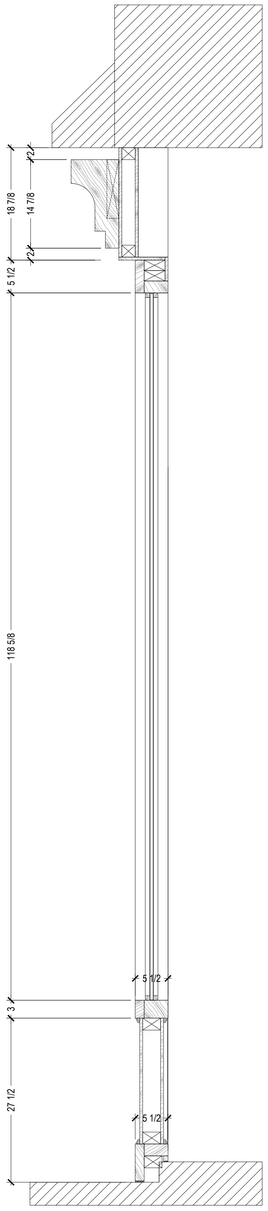


5 SECTION
SCALE: 1"=1'-0"

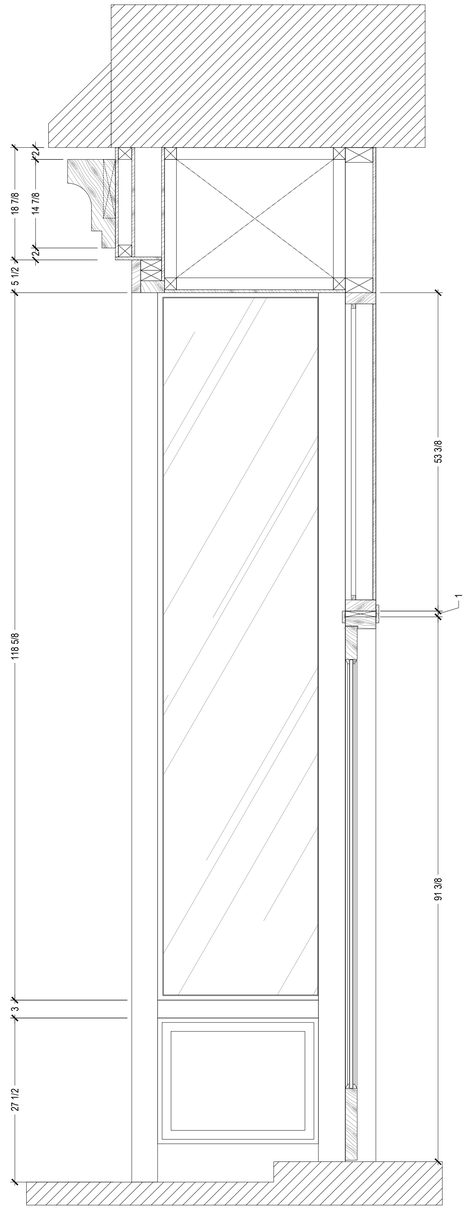


6 SECTION
SCALE: 1"=1'-0"

WD 01
WOOD FRAME
STOREFRONT (AS PER
APPROVED SAMPLE)

PROJECT:

SHOPFRONT
ADDRESS
ADDRESS
ADDRESS

FX-X_TITLE

| REVISIONS | BY |
|---|---|
| | |
| | |

| | |
|---|---|
| ENG: | ---- |
| FIN: | ---- |
| PM: | ---- |
| DATE: | NOV. 06, 2025 |
| JOB # | 00-00-00000 |
| ARCH REF. | T-REF |
| | B-REF |

SHEET
03