THIS IS A TRUSS/COMPONENT PLACEMENT DIAGRAM (TPD) ONLY; NOT AN ENGINEERED DOCUMENT. Trusses are designed as individual buildingcomponents tobe incorporated into the building design at the specification of thebuilding designer. See individual truss design drawings (TDD's) foreach truss design identified on the TPD. The building designer is responsible for temporaryand permanent bracing of the roof and floor system and for the overall structure. The design of the support structure including but not limited to headers, beams, walls, and columns is also the responsibility of the building designer. For general guidance regarding installation and bracing, consult "Building Component Safety Information" (BCSI) available from the SBC Association (www.sbcacomponents.com). It is the responsibility of the General Contractor to verify that the provided component layout matches the final intended construction plans, loading conditions, and use. If they do not, it is the responsibility of the General Contractor to notify UFP and provide plans containing the latest specifications and designs. UFP will not be responsible for plan changes by others after final approval of shop drawings, or for errors or modifications made on-site during construction. DO NOT CUT, NOTCH, DRILL, OR OTHERWISE "REPAIR" MANUFACTURED TRUSSES IN ANY WAY WITHOUT PRIOR WRITTEN AUTHORIZATION BY A LICENSED PROFESSIONAL DESIGNATED BY UFP. The Framer is responsible to verify all dimensions, including adjusting member spacing within tolerances to allow for the drop and rise of plumbing/HVAC, unless noted otherwise. Truss-to-wall connections, if shown, are for uplift only and do not consider lateral loads. All connectors on this project are to be installed per the connector manufacturer's specifications. All connectors shown that are not truss-to-truss are suggestions only and are to be verified by the Building Designer or Engineer of Record for suitability to this particular project. UFP accepts no responsibility for the specific application or suitability of any connector that is not truss-to-truss as they apply to this specific structure.

The following information is an approximate and NOT guaranteed.

ROOF AREA	1566.08
SHEATHING COUNT*	54
OVERHANGE LINES	111.58
RAKED LINES	43.83
RIDGE LINES	24.6
HIP LINES	48.51
VALLEY LINES	0

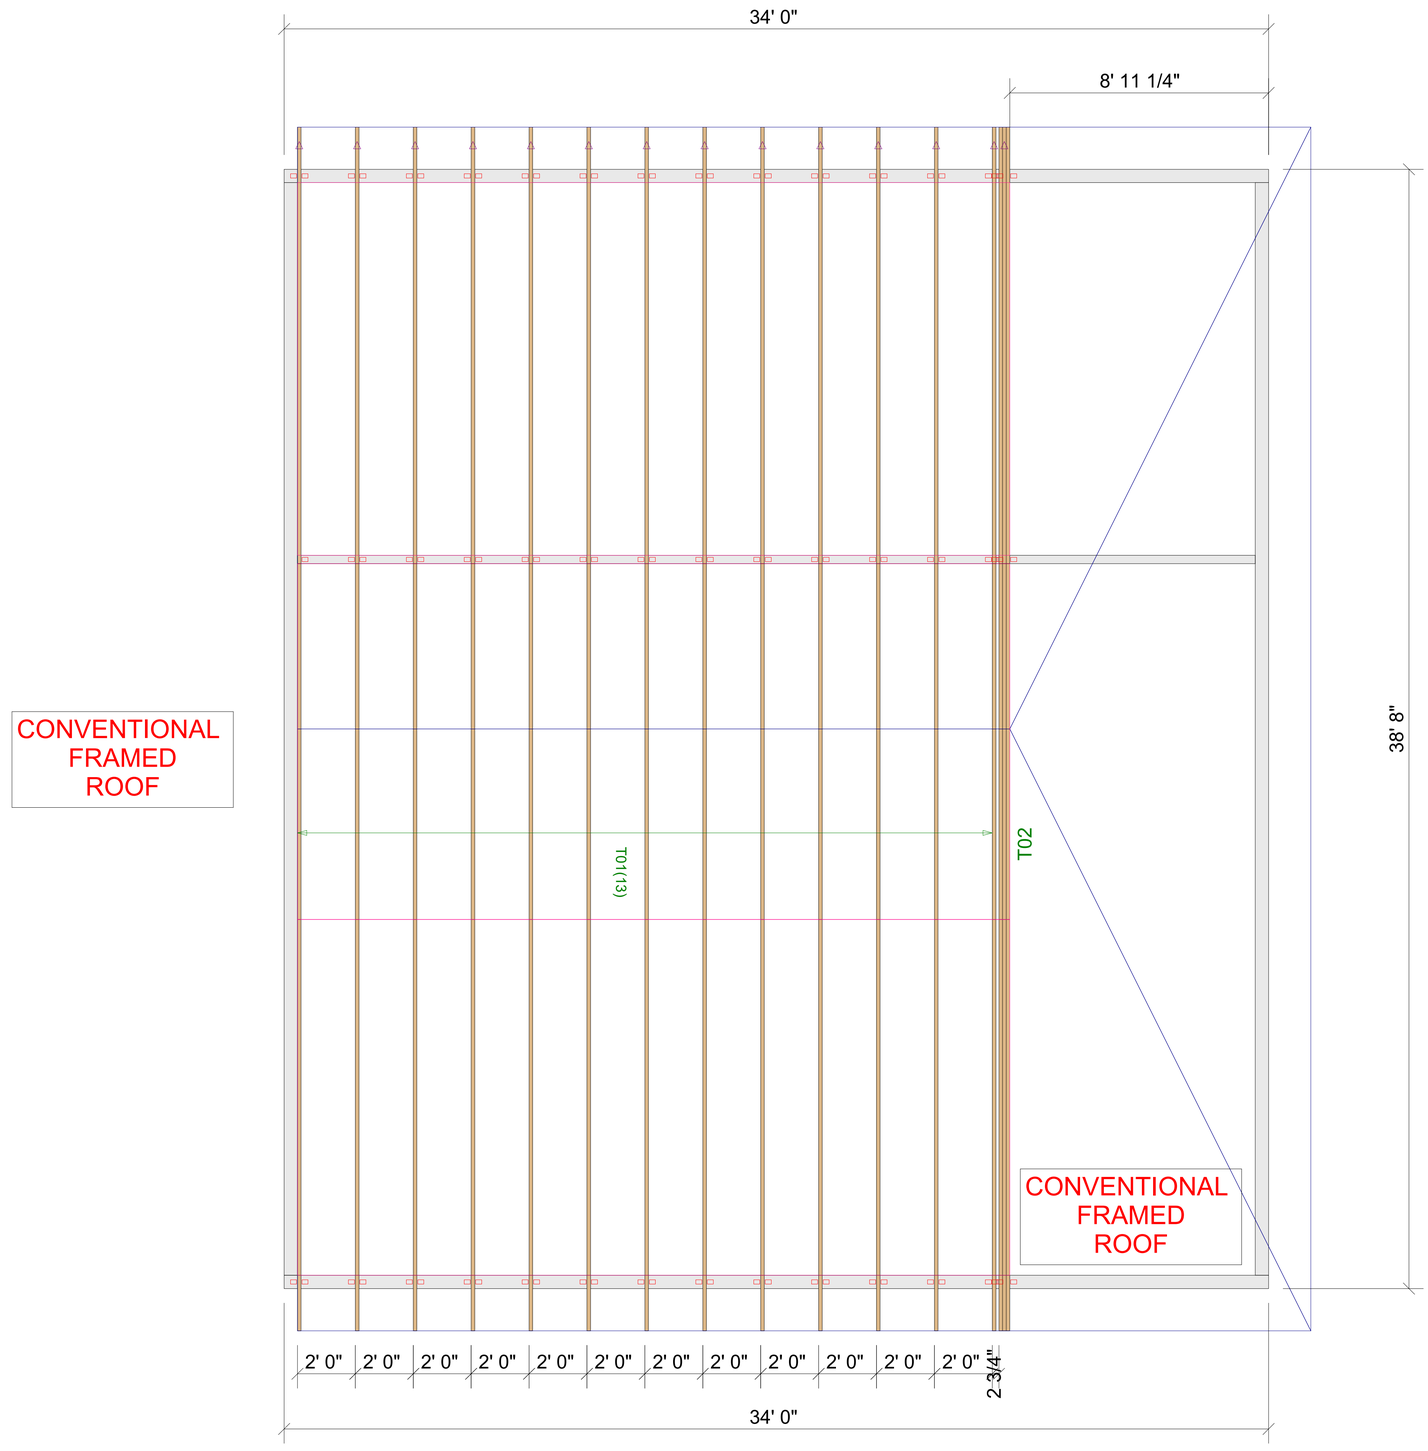

ROOF TRUSS Placement Plan

SCALE: N.T.S.

UFP SITE BUILT
A UFP INDUSTRIES COMPANY

UFP Auburn (315) 253-2758
UFP Chicopee (413) 213-3722
UFP Bertin (856) 767-0043
UFP Gordon (800) 488-2811
UFP Hudson (800) 333-2092
UFP New Windsor (800) 828-2906
UFP Sidney (607) 563-1556
UFP Wilton (603) 824-9690

TRUSSTRAX UFP CONSTRUCTION
TrussTrax.ufpi.com

This drawing is property of UFP Site Built, LLC. Any unauthorized use of this document without written permission is prohibited. UFP relinquishes ownership of delivered product upon delivery. Owner of product must obtain UFP's authorization prior to any alteration or modification of product; UFP will not be held responsible for any unauthorized modifications done or costs incurred without prior written authorization from UFP.

BFS

FIRE HOUSE

SOUTH ORANGETOWN

70 INDEPENDENCE AVE
TAPPAN, NY 10983

REVISIONS		
DATE	DESCRIPTION	DSN
.	.	.
.	.	.
.	.	.
.	.	.
.	.	.
.	.	.
.	.	.
.	.	.

DESIGNER DJB
LAYOUT DATE 10/09/2025
ARCH DATE 09/15/2025
STRUC DATE XX/XX/XX

JOB #: 25100079BR